PLANNING NOTES

1. THE EXTERIOR WALKWAYS AND OUTDOOR DINING AREA OF THE SUBJECT SITE MUST BE POWER WASHED TWICE A MONTH AND COMPLY WITH ALL NATIONAL POLLUTANT DISCHARGE ELIMINATION SYSTEM (NPDES REQUIREMENTS).
2. ALL OUTDOOR FURNITURE WILL BE FASTENED TO THE FLOOR OR BROUGHT INSIDE WHEN THE INDOOR DINING AREA IS CLOSED.
3. THE FAST-FOOD RESTAURANT WILL PROVIDE CONTACTLESS ORDERING VIA A MOBILE ONLINE ORDERING SYSTEM.
4. EMPLOYEES WILL ASSIST WITH DRIVE-THROUGH TRAFFIC MANAGEMENT AND THAT CONES WILL BE USED TO GUIDE VEHICLES IN THE CASE OF TRAFFIC OVERFLOW.
5. AN ANTI-GRAFFITI FINISH SHALL BE UTILIZED ON ALL EXPOSED WALLS UNDER 10 FEET.
6. ALL SIGNAGE WILL BE ISSUED UNDER A SEPARATE PERMIT.
7. THE SUBJECT SITE WILL BE CLEANED OFF AND ALL CONSTRUCTION MATERIALS WILL BE REMOVED AND DISPOSED OF PROPERLY.

PARKING SUMMARY

1. PARKING SPACE REQUIRED: BASIS	34 SPACES 1 STALL PER 150 S.F. OF GROSS FLOOR AREA
BUILDING AREA:	5,108 S.F. /150 S.F. = 34 SPACES
2. PARKING SPACE PROVIDED:	67 SPACES
ACC. SPACES REQUIRED	3 SPACES (2025 CBC TABLE 11B-208)
EV CAPABLE SPACES REQUIRED:	13 SPACES (2025 CALGREEN STANDARD BUILDING CODE TABLE 5.106.5.3.1)
EVCS SPACES REQUIRED:	6 SPACES (2025 CALGREEN STANDARD BUILDING CODE TABLE 5.106.5.3.1)
ACC EVCS SPACE REQUIRED:	1 VAN ACCESSIBLE & 1 STANDARD ACCESSIBLE (2025 CBC TABLE 11B-228.3.2.1)
STANDARD SPACES PROVIDED:	47 SPACES
ACC. SPACES PROVIDED:	4 SPACES (2 VAN ACC.)
EVCS SPACES PROVIDED:	6 SPACES (1 VAN ACC., 1 STANDARD ACC.)
EV CAPABLE (FUTURE) PROVIDED:	7 SPACES (TOTAL INCLUDING 6 EVCS SPACES)
COMPACT SPACES	3 SPACES
3. SHORT TERM & LONG TERM BICYCLES PARKING	
SHORT TERM BICYCLE SPACES REQUIRED: BASIS: 20% OF TOTAL PARKING SPACES	67X 20% = 14 SPACES
SHORT TERM BICYCLE SPACES PROVIDED	7 BIKE RACKS (14 SPACES)
LONG TERM BICYCLE SPACES REQUIRED: BASIS: 10% OF 20 STAFF PARKING STALLS:	2 SPACES
LONG TERM BICYCLE SPACES PROVIDED:	2 SPACES (INSIDE TRASH ENCLOSURE STORAGE ROOM, SEE SHEET A-103)

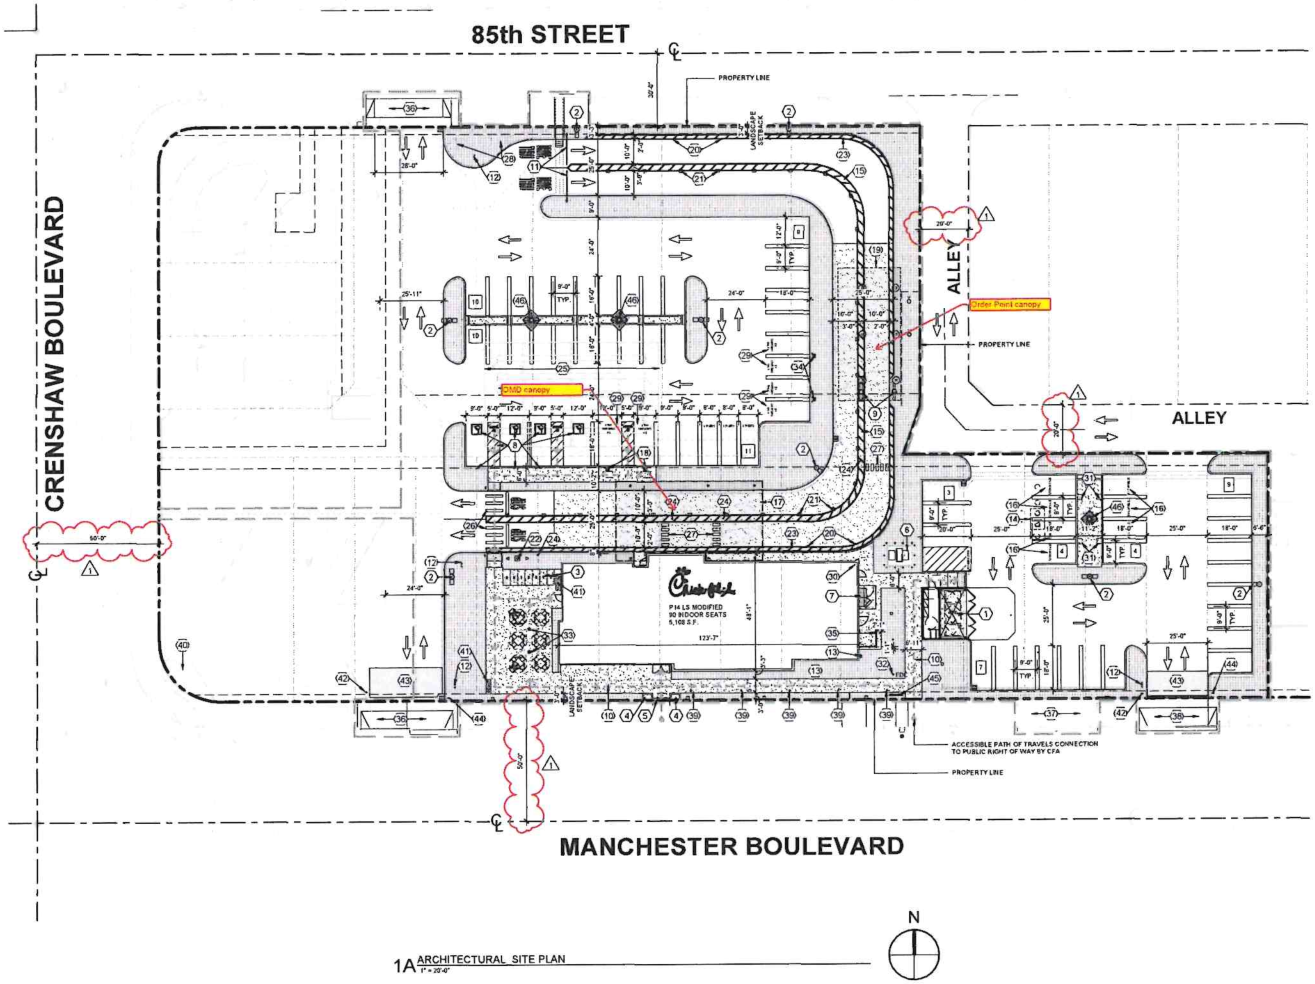

1A ARCHITECTURAL SITE PLAN
1" = 20'-0"

SITE PLAN LEGEND

PROPERTY LINE	━━ ━ ━ ━━
BUILDING LINE	═══
6" CURB & GUTTER	═══
SIDEWALK	░░░
ACCESSIBLE PATH OF TRAVEL	← − − − ← − − −
4" WIDE DIAGONAL STRIPPING	▨
EASEMENT LINE	− − − − − −
CHICK FIL A'S LIMIT OF WORK	— — — —

SITE PLAN KEYNOTES ⬡

1	TRASH ENCLOSURE WITH STORAGE ROOM. RE: 1A/A-103
2	LOT LIGHT. RE: ELECTRICAL
3	SHORT TERM BIKE PARKING, 2 BIKE RACKS (4 SPACES). RE: 4D/A-102
4	LOW PLANTER BEDS
5	STEP DOWN AND RAILING
6	TRANSFORMER PAD. RE: CIVIL & ELECTRICAL PLANS
7	MAIN ELECTRICAL DISTRIBUTION PANEL. RE: ELECTRICAL PLANS
8	ACCESSIBLE SPACES, STRIPING, SIGNAGE AND RAMPS. RE: CIVIL PLANS
9	DRIVE-THRU MENU BOARDS, UNDER SEPARATE PERMIT. SEE SIGNAGE PACKAGE
10	CONCRETE SIDEWALK. RE: CIVIL PLANS
11	HEIGHT CLEARANCE ARM, UNDER SEPARATE PERMIT. SEE SIGNAGE PACKAGE
12	DIRECTIONAL SIGN. UNDER SEPARATE PERMIT. SEE SIGNAGE PACKAGE
13	GAS METER. RE: CIVIL PLANS
14	GREASE INTERCEPTOR. RE: PLUMBING AND CIVIL PLANS
15	3'-0" STRIPED WALKWAY FOR TEAM MEMBER. RE: CIVIL PLANS
16	EV CAPABLE STALL. RE: ELECTRICAL PLANS
17	OUTSIDE MEAL DELIVERY CANOPY BY OWNER, UNDER SEPARATE PERMIT. RE: 1A/A-105
18	SINGLE EV CHARGING STATION. RE: ELECTRICAL PLANS
19	ORDER POINT CANOPY BY OWNER, UNDER SEPARATE PERMIT. RE: 1A/A-104
20	SAFETY POST AND MOUNT WITH MAGNETIC DELINEATOR BASE MAX. 20-0" SPACING
21	MOVEABLE DELINEATOR WITH RUBBER BASE MAX. 15-0" SPACING
22	FLAG POLE BY OWNER, UNDER SEPARATE PERMIT. RE: SIGNAGE PACKAGE
23	2'-0" STRIPED WALKWAY FOR TEAM MEMBER. RE: CIVIL PLANS
24	TEAM MEMBER CROSSING FLEX SIGN
25	UNDERGROUND DETENTION PIPES. RE: CIVIL PLANS
26	6'-0" W. STRIPED CROSSWALK. RE: CIVIL PLANS
27	3'-0" W. STRIPED CROSSWALK. RE: CIVIL PLANS
28	STORMWATER PUMP. RE: CIVIL PLANS
29	EVCS PARKING SPACE. RE: ELECTRICAL PLANS
30	FIRE RISER
31	FUTURE EV CHARGER. RE: ELECTRICAL PLANS
32	FIRE DEPARTMENT CONNECTION. RE: CIVIL PLANS
33	PEDESTRIAN LIGHT. RE: ELECTRICAL PLANS
34	DUAL EV CHARGING STATION. RE: ELECTRICAL PLANS
35	CART CORRAL ENCLOSURE. RE: 1B/A-106
36	EXISTING DRIVEWAY TO BE REMOVED. CONSTRUCT NEW DRIVEWAY PER CITY STANDARD. RE: CIVIL
37	EXISTING DRIVEWAY TO BE REMOVED. CONSTRUCT NEW SIDEWALK PER CITY STANDARD. RE: CIVIL
38	NEW DRIVEWAY PER CITY STANDARDS. RE: CIVIL
39	BOLLARD LIGHT. RE: ELECTRICAL PLANS
40	EXISTING PYLON SIGN - TO BE REFINISHED & RESURFACED. UNDER SEPARATE PERMIT
41	TRASH RECEPTACLES. RE: A-102 PATIO FLOOR PLAN & SCHEDULE
42	NO LEFT TURN SIGN, UNDER SEPARATE PERMIT. SEE SIGNAGE PACKAGE
43	EXPOSED AGGREGATE CONCRETE (POOR MAN'S TERRAZZO) PAVING, SAW CUT CONTROL JOIST @ 6'-0" O.C.
44	ACCESSIBLE DRIVEWAY ENTRANCE SIGN, UNDER SEPARATE PERMIT. SEE SIGNAGE PACKAGE
45	DOUBLE CHECK DETECTOR ASSEMBLY PER CITY OF INGLEWOOD WATER STANDARDS. RE: CIVIL
46	ADA-APPROVED TREE GRATE WITH NARROW GROVES FLUSH WITH THE PAVING SURFACE

Chick-fil-A
5200 Buffington Road
Atlanta, Georgia
30349-2998

crho
architects
1833 E. 17th Street
3rd Floor - Suite 301
Santa Ana, CA 92705
Phone 714.832.1834

CHICK-FIL-A
Crenshaw & Manchester

3003 W. MANCHESTER BLVD.
INGLEWOOD, CA 90305

FSR#06271

BUILDING TYPE / SIZE	Mod. P14 LS BASE
RELEASE	26.B2
PRINTED FOR	

Permit

REVISION SCHEDULE

NO.	DATE	DESCRIPTION
1	9/25/26	AGENCY REVISION

Permit

CONSULTANT PROJECT #	25-132
DATE	6/5/26
DRAWN BY	K.N.

SHEET
ARCHITECTURAL SITE PLAN

SHEET NUMBER
A-101